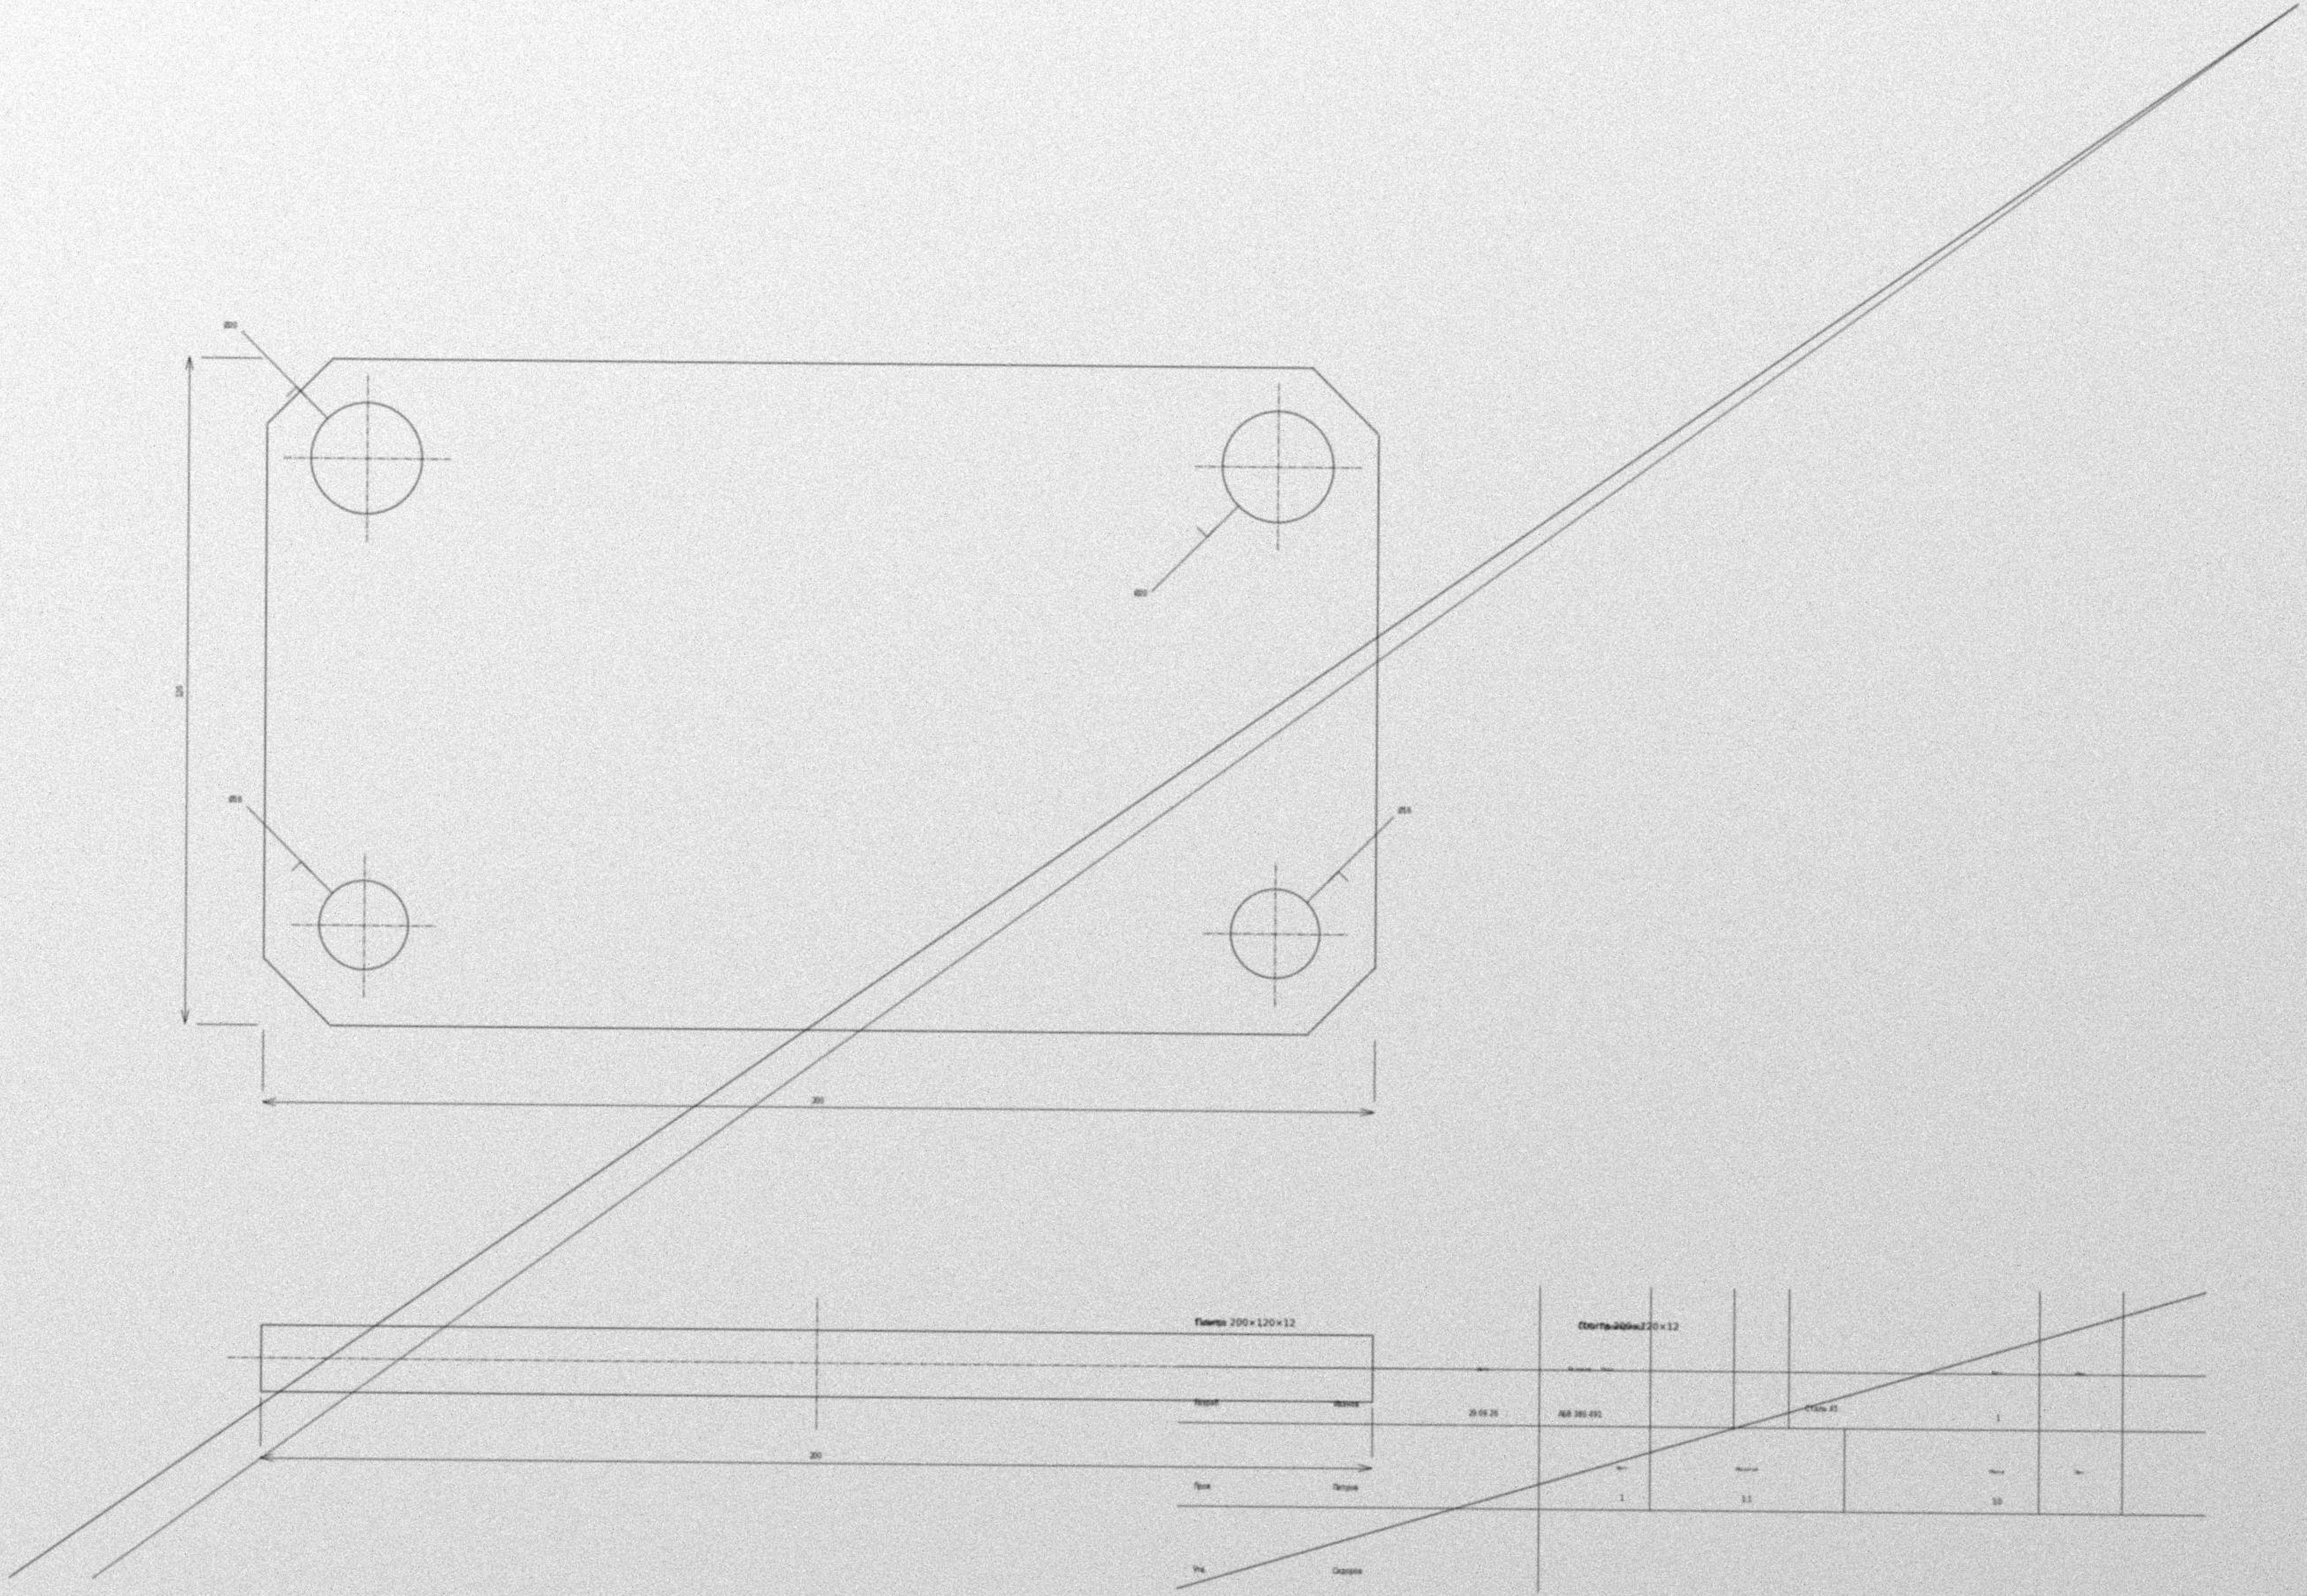
Ø20
Ø20
120
Ø16
Ø16
200
200
Плита 200×120×12
Плита 200×120×12
Разраб
Иванов
Пров
Петров
Утв
Сидоров
20.09.26
АБВ 380.491
Сталь 45
1
1
1:1
10