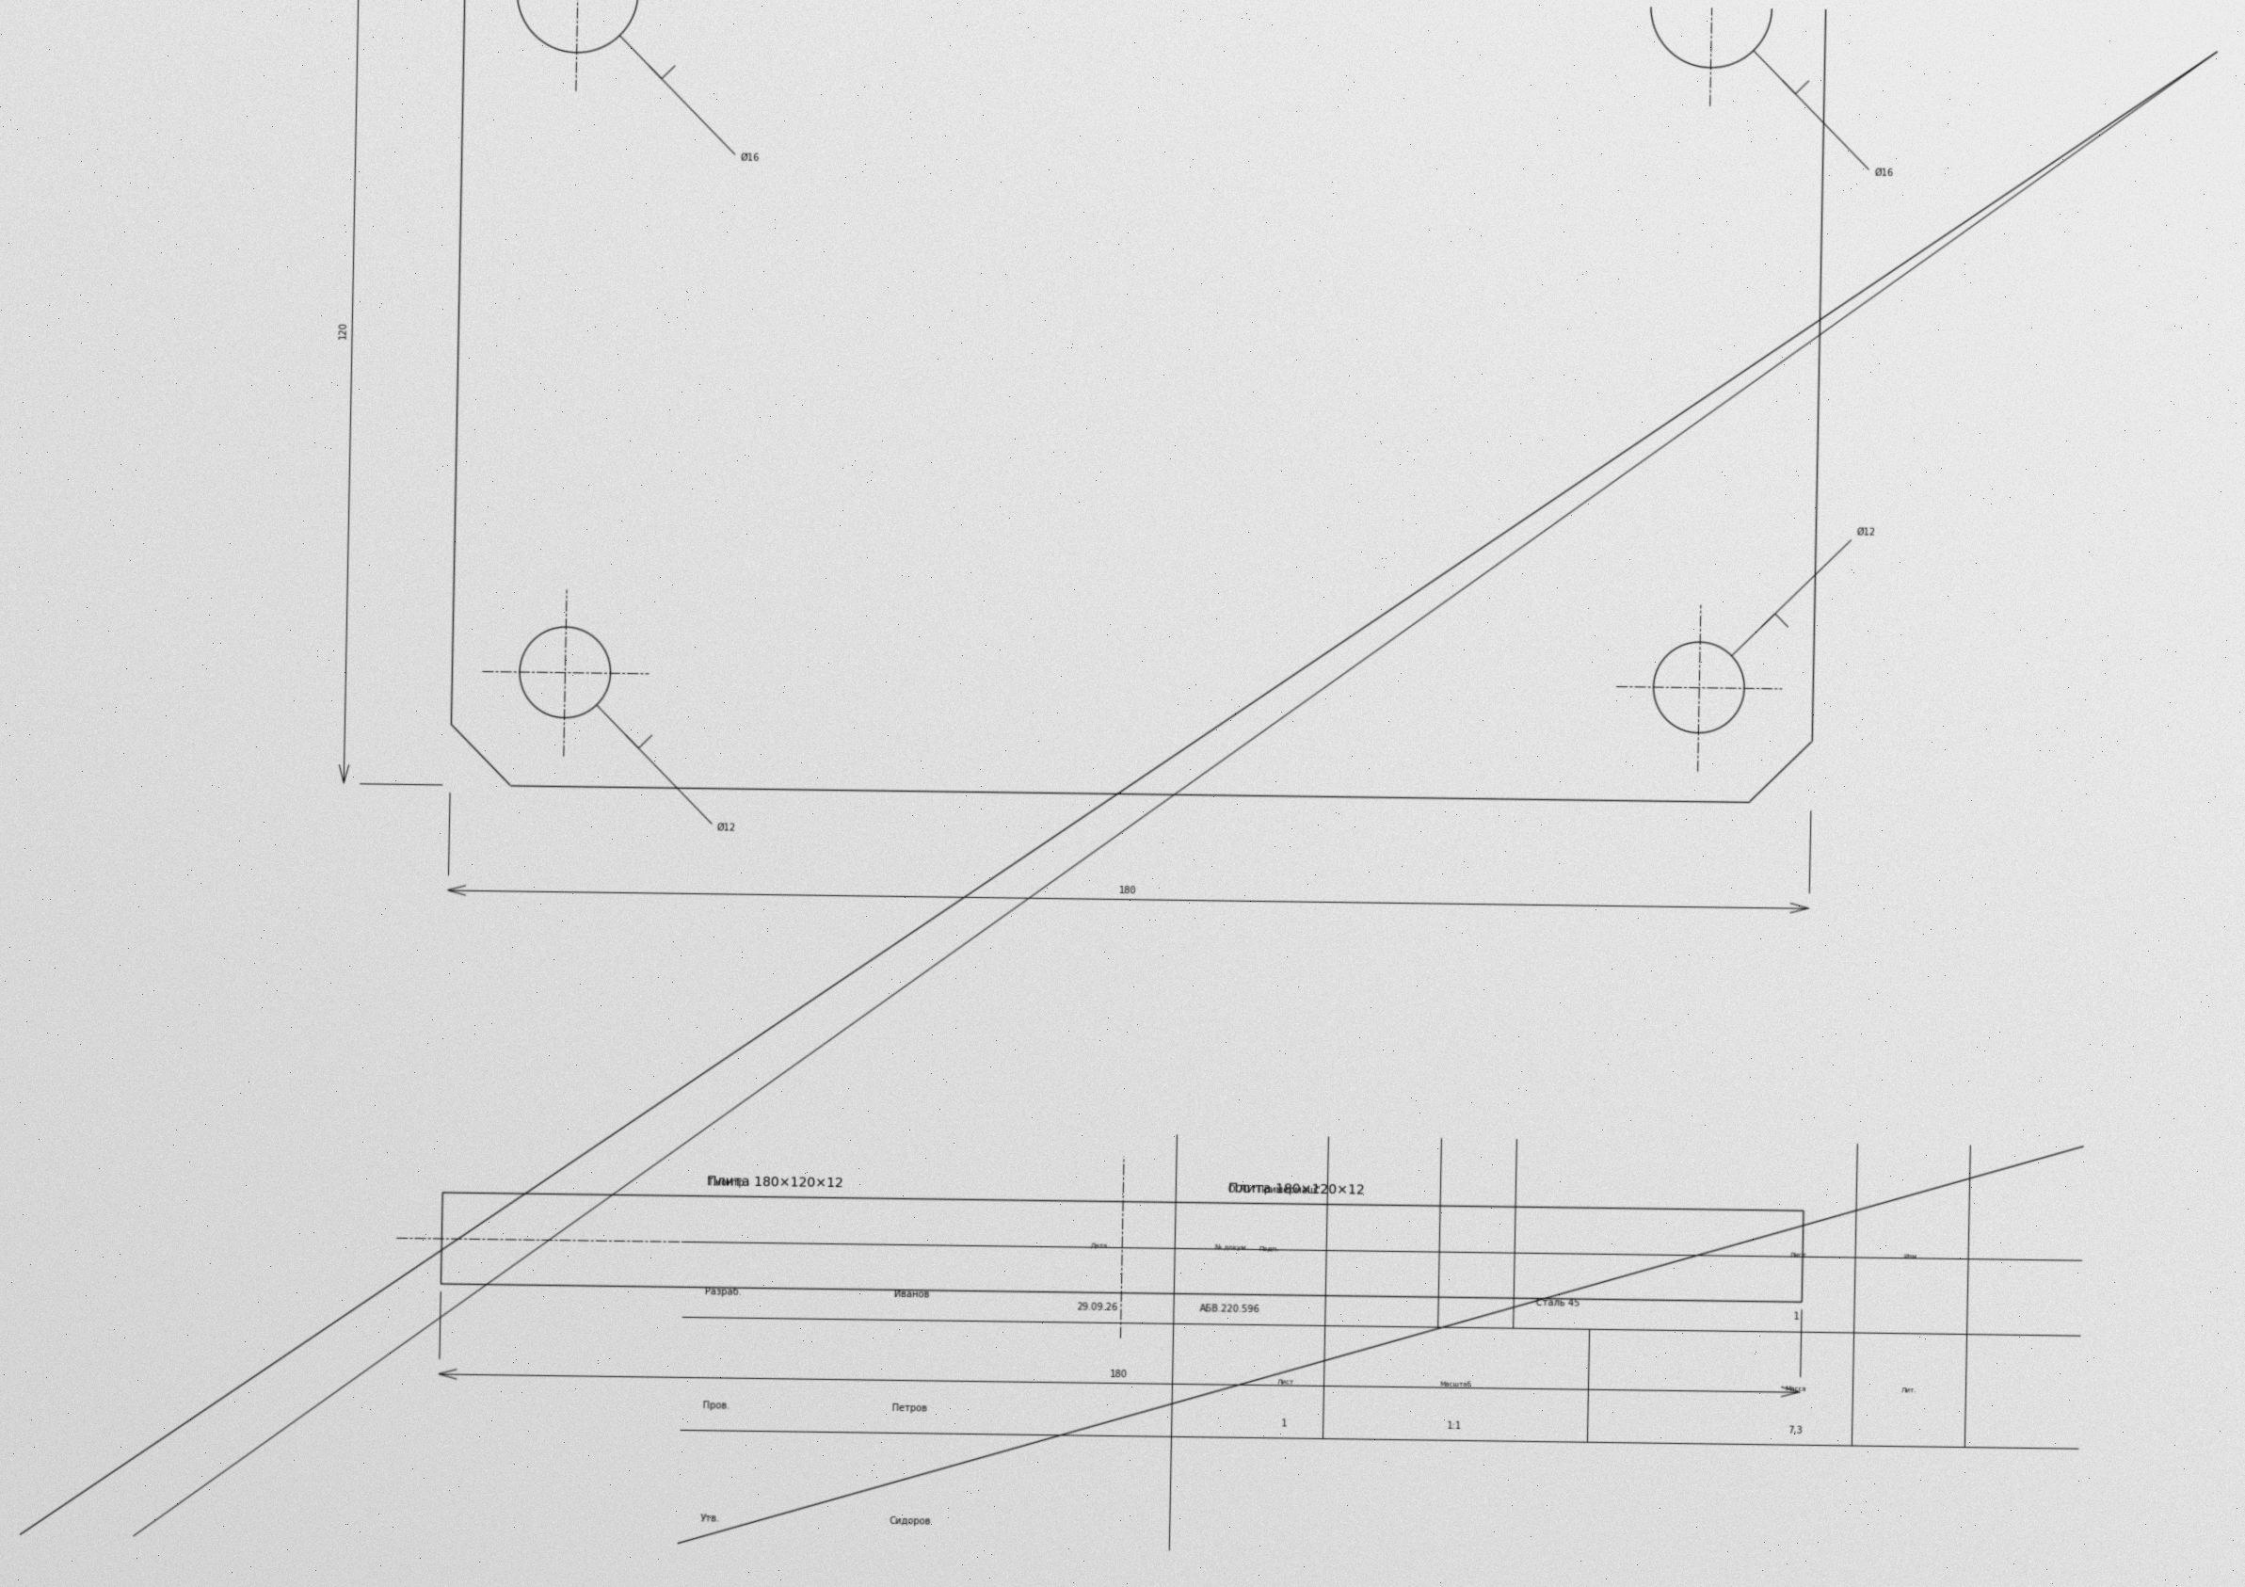

Ø16
Ø16
120
Ø12
Ø12
180
Плита 180×120×12
Плита 180×120×12
Разраб.
Иванов
29.09.26
АБВ.220.596
Сталь 45
1
180
Пров.
Петров
1
1:1
7,3
Утв.
Сидоров.